


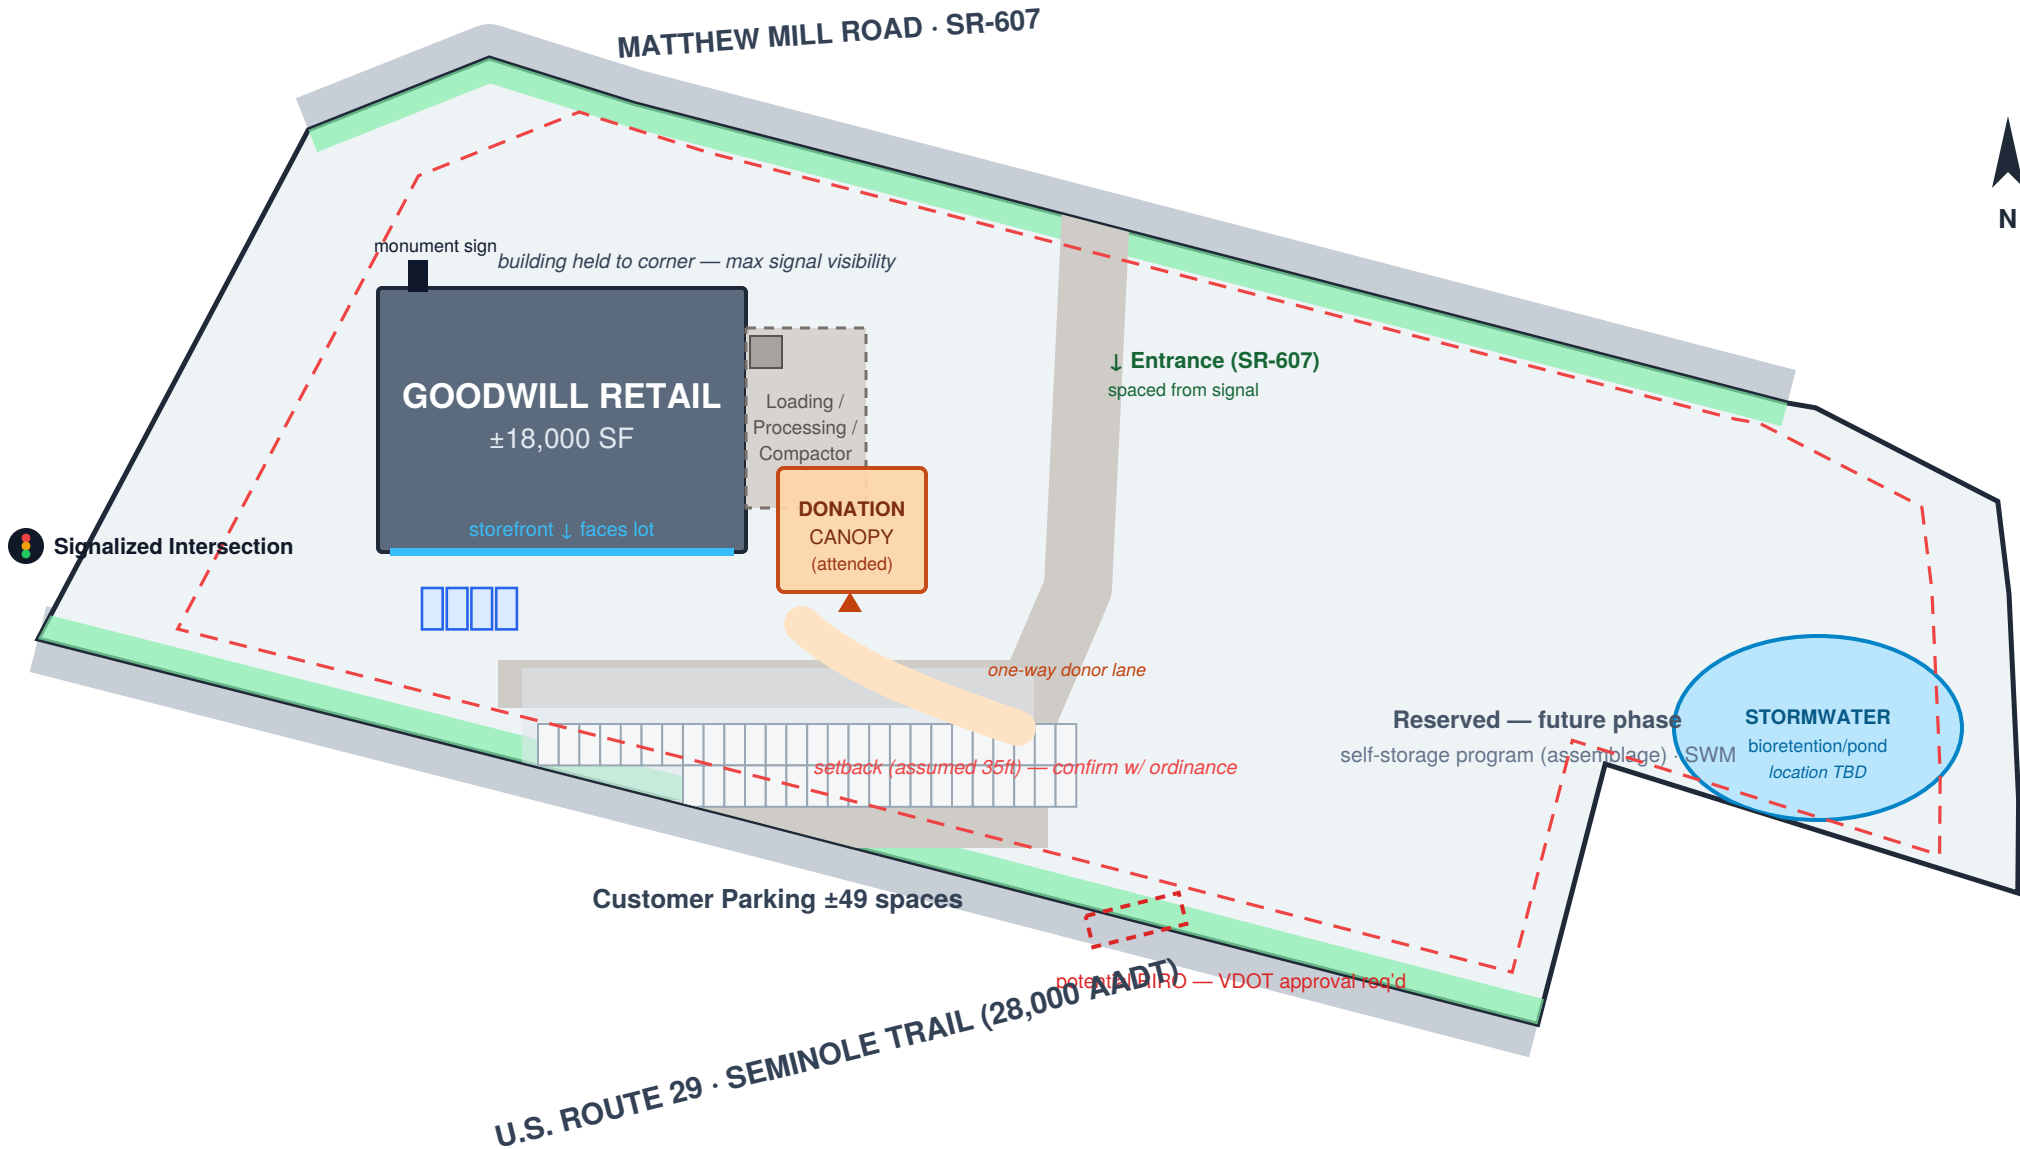

Goodwill — Conceptual Site Test-Fit

6968 Seminole Trail · Ruckersville, VA 22968
Greene County · TMP 66-A-46 & 66-A-45

SITE DATA

Gross site (per 2023 survey)	±5.04 ac
GIS polygon computes to	4.85 ac
Assessment / CAMA record	2.32 ac
Current zoning	R-1 / R-2
Flood zone (FIRM 5107020200)	None

PROGRAM (illustrative)

Building footprint	±18,000 SF
Parking provided	±49 spaces
Parking required (1/250–1/200)	72–90
Attended donation canopy	yes
Loading / processing / SWM	yes
Est. impervious coverage	~30–35%
Verdict	FITS — ample room

OPEN ITEMS / TO CONFIRM

- 50 spaces is UNDER typical req for 18k SF
— right-sized for a ~12,500 SF store, or hold 18k & seek a reduced-ratio approval
- Rezoning R-1 → commercial (legislative; FLU corridor supports the case)
- VDOT access — likely entrance off SR-607; US-29 restricted (RIRO at best)
- Acreage mismatch: 2.32 vs 4.85 vs 5.04 ac
— resolve before pricing @ \$1.475M/ac
- 3 existing dwellings to be razed
- Greene Co. setbacks + parking ratio (used placeholders)
- Goodwill prototype criteria (used typical)

LEGEND

- Building
- Parking
- Donation canopy
- Stormwater

CONCEPTUAL — NOT FOR CONSTRUCTION

Schematic feasibility test-fit. Not a survey, engineered plan, or VDOT/site-plan approval. Prepared for Triangle Investments, internal use.